


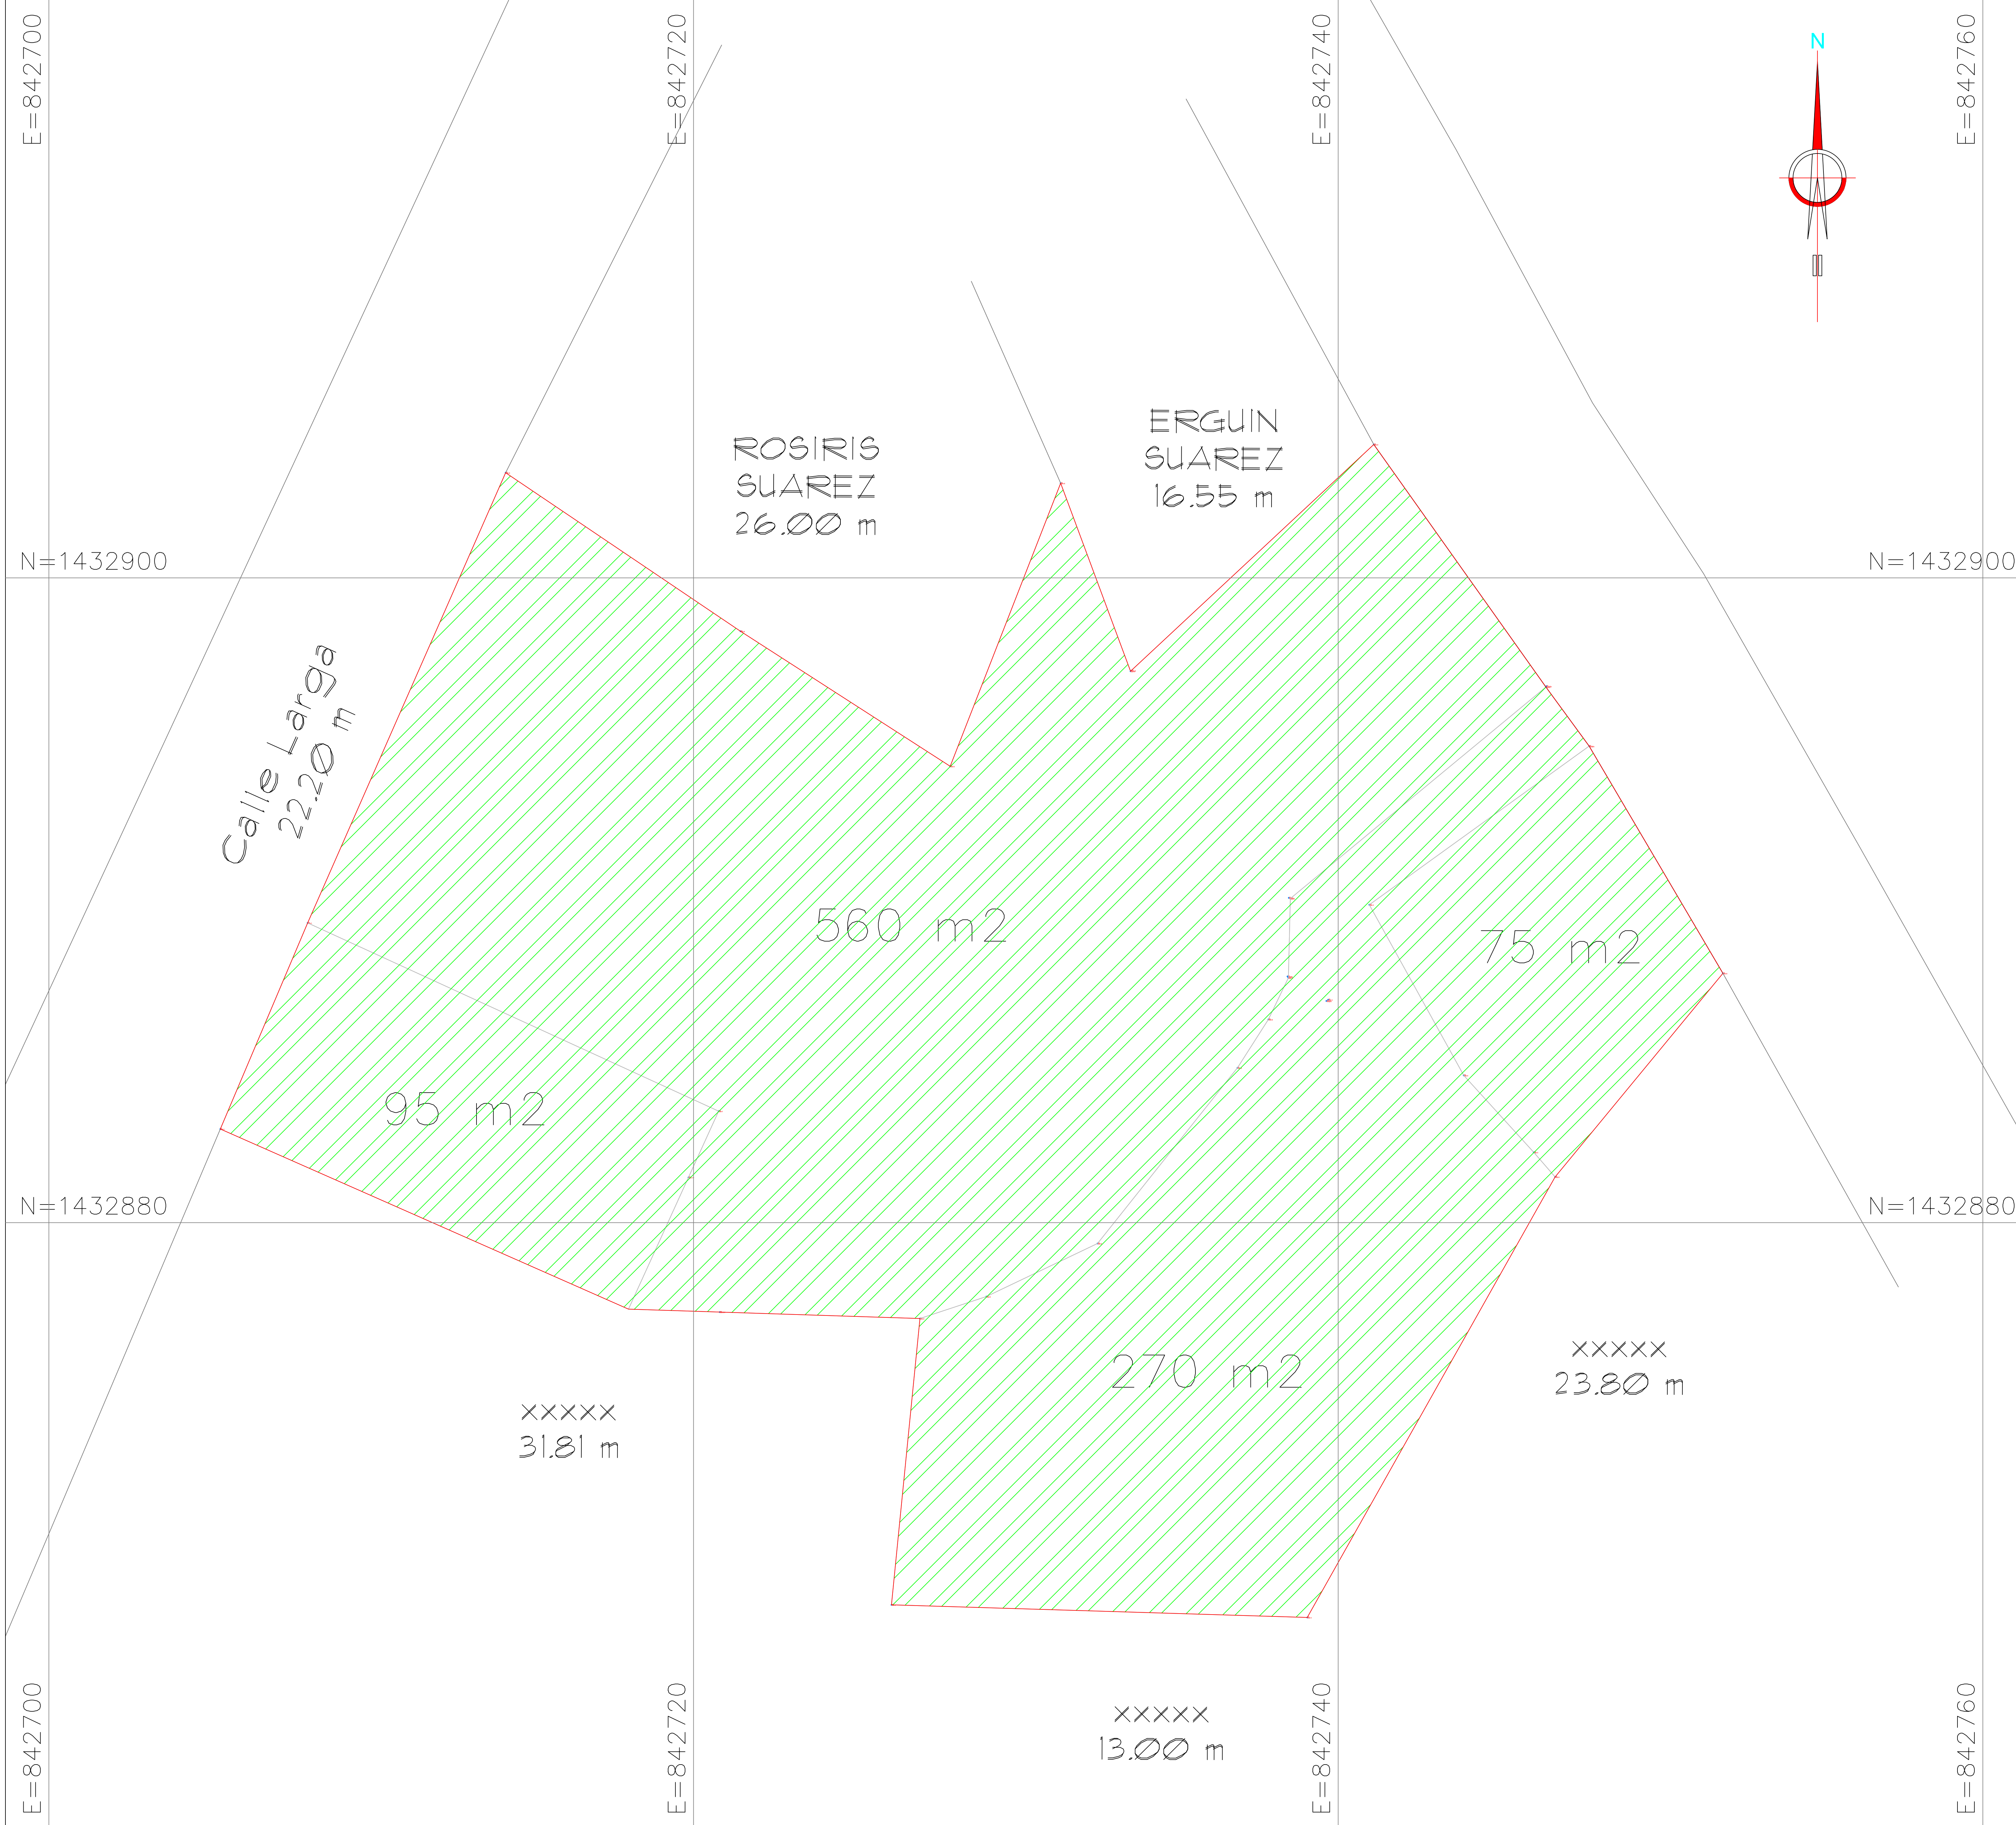



República de Colombia
Departamento de Córdoba
Municipio de Pueblo Nuevo
Plano Georreferenciado

INFORMACIÓN DEL PREDIO		COORDENADAS COLINDANTES	
Propietario: PEDRO ANTONIO AVILEZ DIAZ Predio: Urbano Nro_Mat: 148-23391 Ced_Catastral: 01-00-000-0001 Direccion: k 11 19 A Área_Terreno: 1000 m2	PUNTO	ESTE	NORTE
	1	848610.738	1429603.630
	2	848890.087	1429184.061
	3	848884.998	1429159.884
	4	848492.747	1429274.088
CONVENCIONES			
PUNTOS			
PREDIO			
CATASTRAL			


DESCRIPCIÓN DEL PREDIO
PREDIO QUE CONSTA DE UNA EXTENSIÓN SUPERFICIAL DE 1000 m2 ENCERRADO DENTRO LOS SIGUIENTES LINDEROS:
NORTE: En medida
ESTE: En medida de
SUR: En medida de
OESTE: En medida de

GEORREFERENCIACION


OSCAR ANDRES PAYARES ACEVEDO
M.P 01-19653 CPNT
Fuente Cartográfica: PROPIA
Fuente : Levantamiento planimetrico
Fecha: Mayo 2026



Información de Referencia Espacial
Sistema de Coordenadas: MAGNA_SIRGAS_Colombia Origen Bogota
Sistema de Referencia de Coordenadas (CRS): EPSG: 3116
Proyección Cartográfica: Universal Transversal Mercator

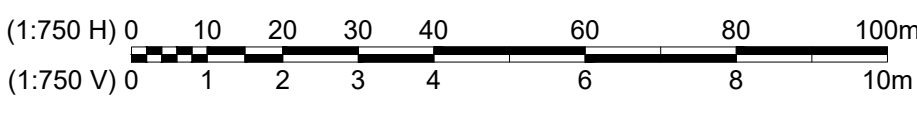Escala:1:75


UBICACIÓN: Municipio de Pueblo Nuevo - Córdoba



PLANO
1/1